

LISTA DE MATERIALES


PARTE	CANT.	DESCRIPCION	MODELO	MARCA
01	REQ	TUBO DE ALUMINIO 1"	- - - - -	- - - - -
02	01	SELLO DE ALUMINIO DE 1"	EYS-31	CROUSE HINDS
03	01	REDUCCIÓN BUSHING DE 1" A 3/4"	RE-21	CROUSE HINDS
04	01	NIPLE DE 3/4"	NIPLE-2 L	CROUSE HINDS
05	01	CONDULET DE ALUMINIO APEX DE 3/4" TIPO "B"	GRUB-26	APPLETON
06	03	TAPÓN DE ALUMINIO DE 3/4"	PLG-2	CROUSE HINDS
07	REQ	TUBO DE ALUMINIO 3/4"	- - - - -	- - - - -
08	01	COPLE DE ALUMINIO 3/4"	- - - - -	- - - - -
09	01	COPLE FLEXIBLE A PRUEBA DE EXPLOSIÓN DE 1/2" X 18"	ECGJH 118	CROUSE HINDS
10	01	SELLO DE ALUMINIO 1/2"	EYS-11	CROUSE HINDS
11	01	TUERCA UNIÓN MACHO - HEMBRA 1/2"	UNY-105 SA	CROUSE HINDS
12	01	NIPLE DE ALUMINIO 1/2"	NIPLE-2 L	CROUSE HINDS
13	02	REDUCCIÓN BUSHING DE 3/4" a 1/2"	RE-31	CROUSE HINDS
20	03	UNICANAL 4" X 2"	- - - - -	ANCLO
21	01	PLACA DE ACERO DE 9.5" X 9.5" X 3/8"	- - - - -	- - - - -
22	01	TUBO DE ACERO DE 4" CED. 40	- - - - -	- - - - -
23	02	ABRAZADERA TIPO "U" DE 4"	- - - - -	ANCLO
24	04	CARTABÓN DE PLACA DE ACERO DE 5-1/2" X 2" X 1/4"	- - - - -	- - - - -
25	REQ	JUEGO DE TUERCAS Y ARANDELA PLANA DE 1/2"Ø C. STD.	- - - - -	- - - - -
26	01	PLACA DE ACERO DE 6" X 5" X 1/4"	- - - - -	- - - - -
27	REQ	JUEGO DE TORNILLOS DE 5/16" X 1-1/2" LONG. CON TUERCAS Y ARANDELA PLANA CUERDA STD.	- - - - -	- - - - -
28	01	PLACA DE ACERO DE 7" X 7" X 1/4"	- - - - -	- - - - -
29	03	ABRAZADERA 3/4" PARA UNICANAL	- - - - -	- - - - -

LISTA DE EQUIPOS


PARTE	CANT.	DESCRIPCION	MODELO	MARCA
30	01	TRANSMISOR DE GAS	UD-10	DET-TRONICS
31	01	SENSOR DE GAS DE HIDROCARBUROS	PIR-4000	DET-TRONICS

ALTURA DE POSTES


DETECTOR	ALTURA	UBICACIÓN
DME-01	3200 mm	VÁLVULA
DME-02	3000 mm	VÁLVULA
DME-03	3500 mm	---
DME-04	3000 mm	---
DME-05	3000 mm	---
DME-06	3000 mm	---
DME-07		CUARTO DE BATERÍAS
DME-08	3000 mm	TABLERO
DME-09		---

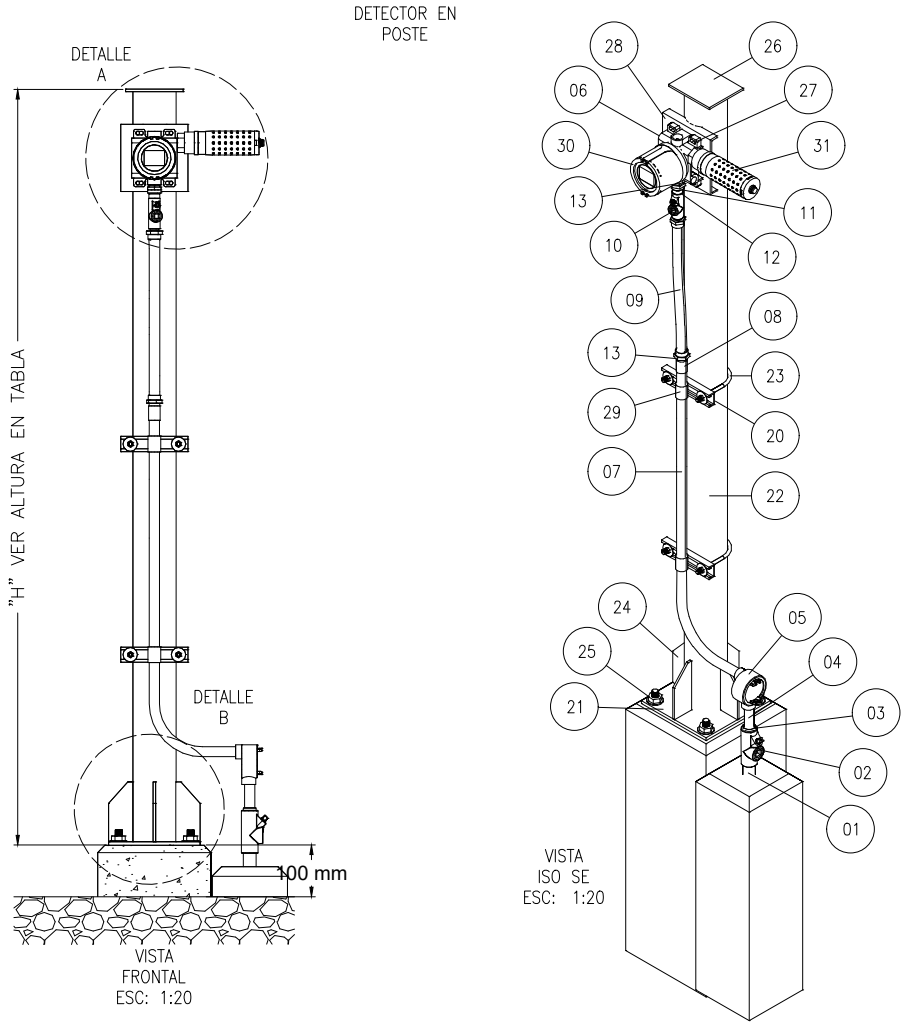

BASE DE CONCRETO FC'=250 kg/cm2
AGREGADO MAXIMO DE 3/4" PLG REFORZADO
CON ANILLOS DE ALAMBRO, FABRICADO
EN OBRA

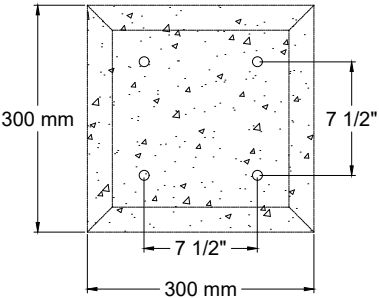



4 ANCLAS DE 1/2" PLG GALVANIZADO
CON TUERCA Y ROLDANA

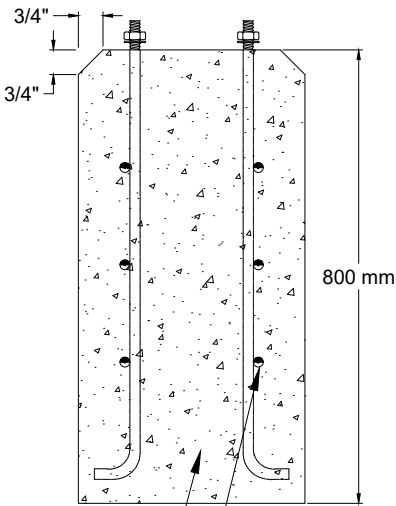

BASE DE CONCRETO DE 300 X 300 X 800 MM
(NIVELAR DE ACUERDO A PISO TERMINADO)

ARMAZON DE ANILLOS DE ALAMBRO DE 3/8" CADA 100 MM

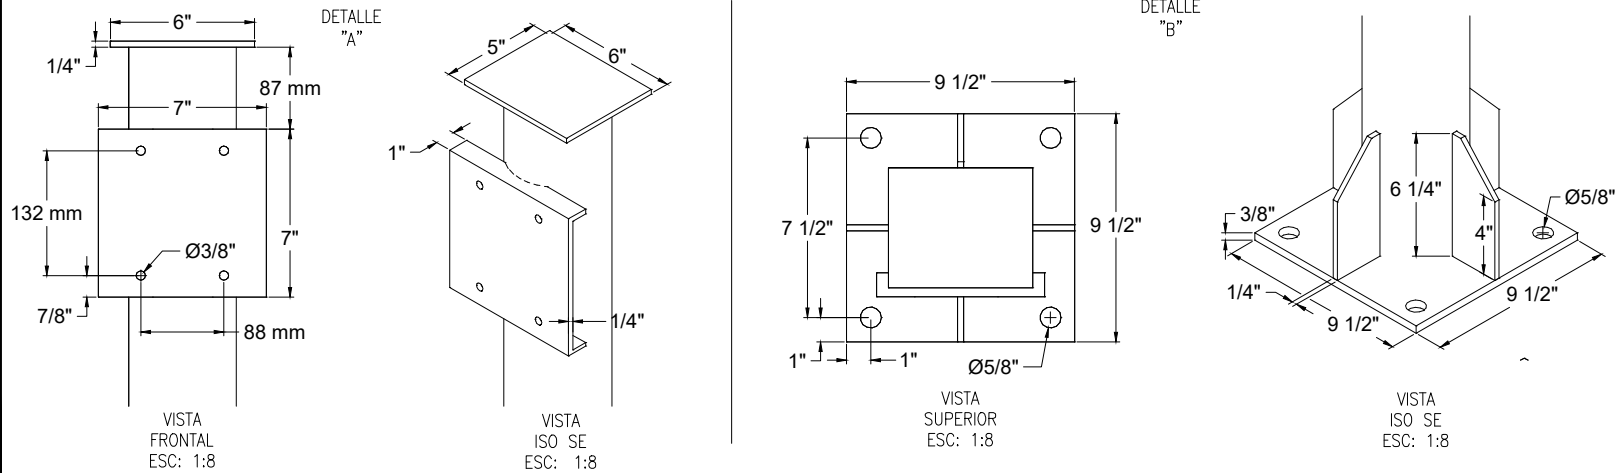

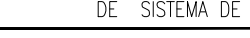R E V I S I O N									DIBUJOS DE REFERENCIA					 GASODUCTO – EL CARRIZO KM 72 + 105	 INTEGRACIONES Y AUTOMATIZACIÓN HOH SA DE CV Del Rosal No. 69 Col. Bosque de los Remedios Naucalpan, Estado de México, CP 53030	"SUMINISTRO, INSTALACIÓN, CONFIGURACIÓN Y PUESTA EN MARCHA DE SISTEMA DE GAS Y FUEGO EN EL CARRIZO"							
REV	DESCRIPCION	DIBUJO	PROY.	REVISO	COORD.	APROBO	CLIENTE	FECHA	No. DIBUJO	DESCRIPCION	DIBUJO	REVISO	FECHA										
A	EMITIDO PARA DISEÑO	DMR	HPP	HGP	–	–	–	FEB/2022															
1	EMITIDO PARA CONSTRUCCIÓN																						
0	AS BUILT																						
														GASODUCTO – EL CARRIZO		Del Rosal No. 69 Col. Bosque de los Remedios Naucalpan, Estado de México, CP 53030		ESC: 1:20, 1:20		No. DE PLANO:		REV.	
														KM 72 + 105		UNIDADES: MM		CRZ–SGYF–DW–15		01 DE 01		A	