



CFE
Comisión Federal de Electricidad





SUMINISTRO, INSTALACIÓN, CONFIGURACIÓN Y PUESTA EN MARCHA
SISTEMA DE TELECOMUNICACIONES

UBICACIÓN DEL GABINETE


ESC:	1:30
UNIDADES:	MM

No. DE PLANO:

01 DE 04

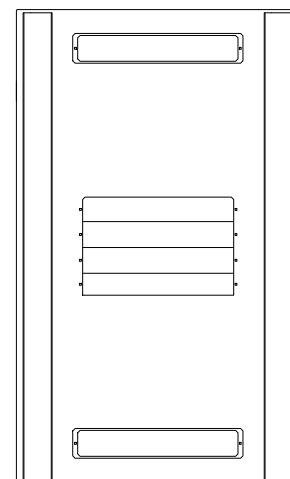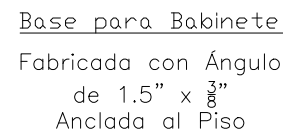


ITEMS	CANT.	DESCRIPCION	MODELO	MARCA
01	03	Servidor PowerEdge	R-450	DELL
02	01	Servidor HPE ProLiant	DL160-G-10	HEWLETT PACKARD
03	02	Switch	C1000-24T-4G-L	CISCO
04	01	KVM Switch, 8 Puertos con Menú	B042-008	TRIPPLITE
05	01	Multicontacto	1PH-15A-08-515RF-15	JAGUAR
06	01	Panel de ventilación triple, 117VAC	VNG-117M-3	DERRANT
07	01	Servidor ProLiant	DL160-G-10	HEWLETT PACKARD
08	01	Gabinete de 1000 x 600 mm	10340	DERRANT

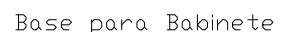


R E V I S I O N									DIBUJOS DE REFERENCIA					 Comisión Federal de Electricidad MEXICO		 INTEGRACIONES Y AUTOMATIZACIÓN HOH SA DE CV		SUMINISTRO, INSTALACIÓN, CONFIGURACIÓN Y PUESTA EN MARCHA		
REV	DESCRIPCION	DIBUJO	PROY.	REVISO	COORD.	APROBO	CLIENTE	FECHA	No. DIBUJO	DESCRIPCION	DIBUJO	REVISO	FECHA					SISTEMA DE TELECOMUNICACIONES		
A	EMITIDO PARA DISEÑO	DMR	HPP	HGP	-	-	-	ABRIL/2023							GABINETE					
1	EMITIDO PARA CONSTRUCCIÓN																			
0	AS BUILT																			
															ESC: 1:16					
															UNIDADES: MM					
																No. DE PLANO: 02 DE 04				

ARQUITECTURA

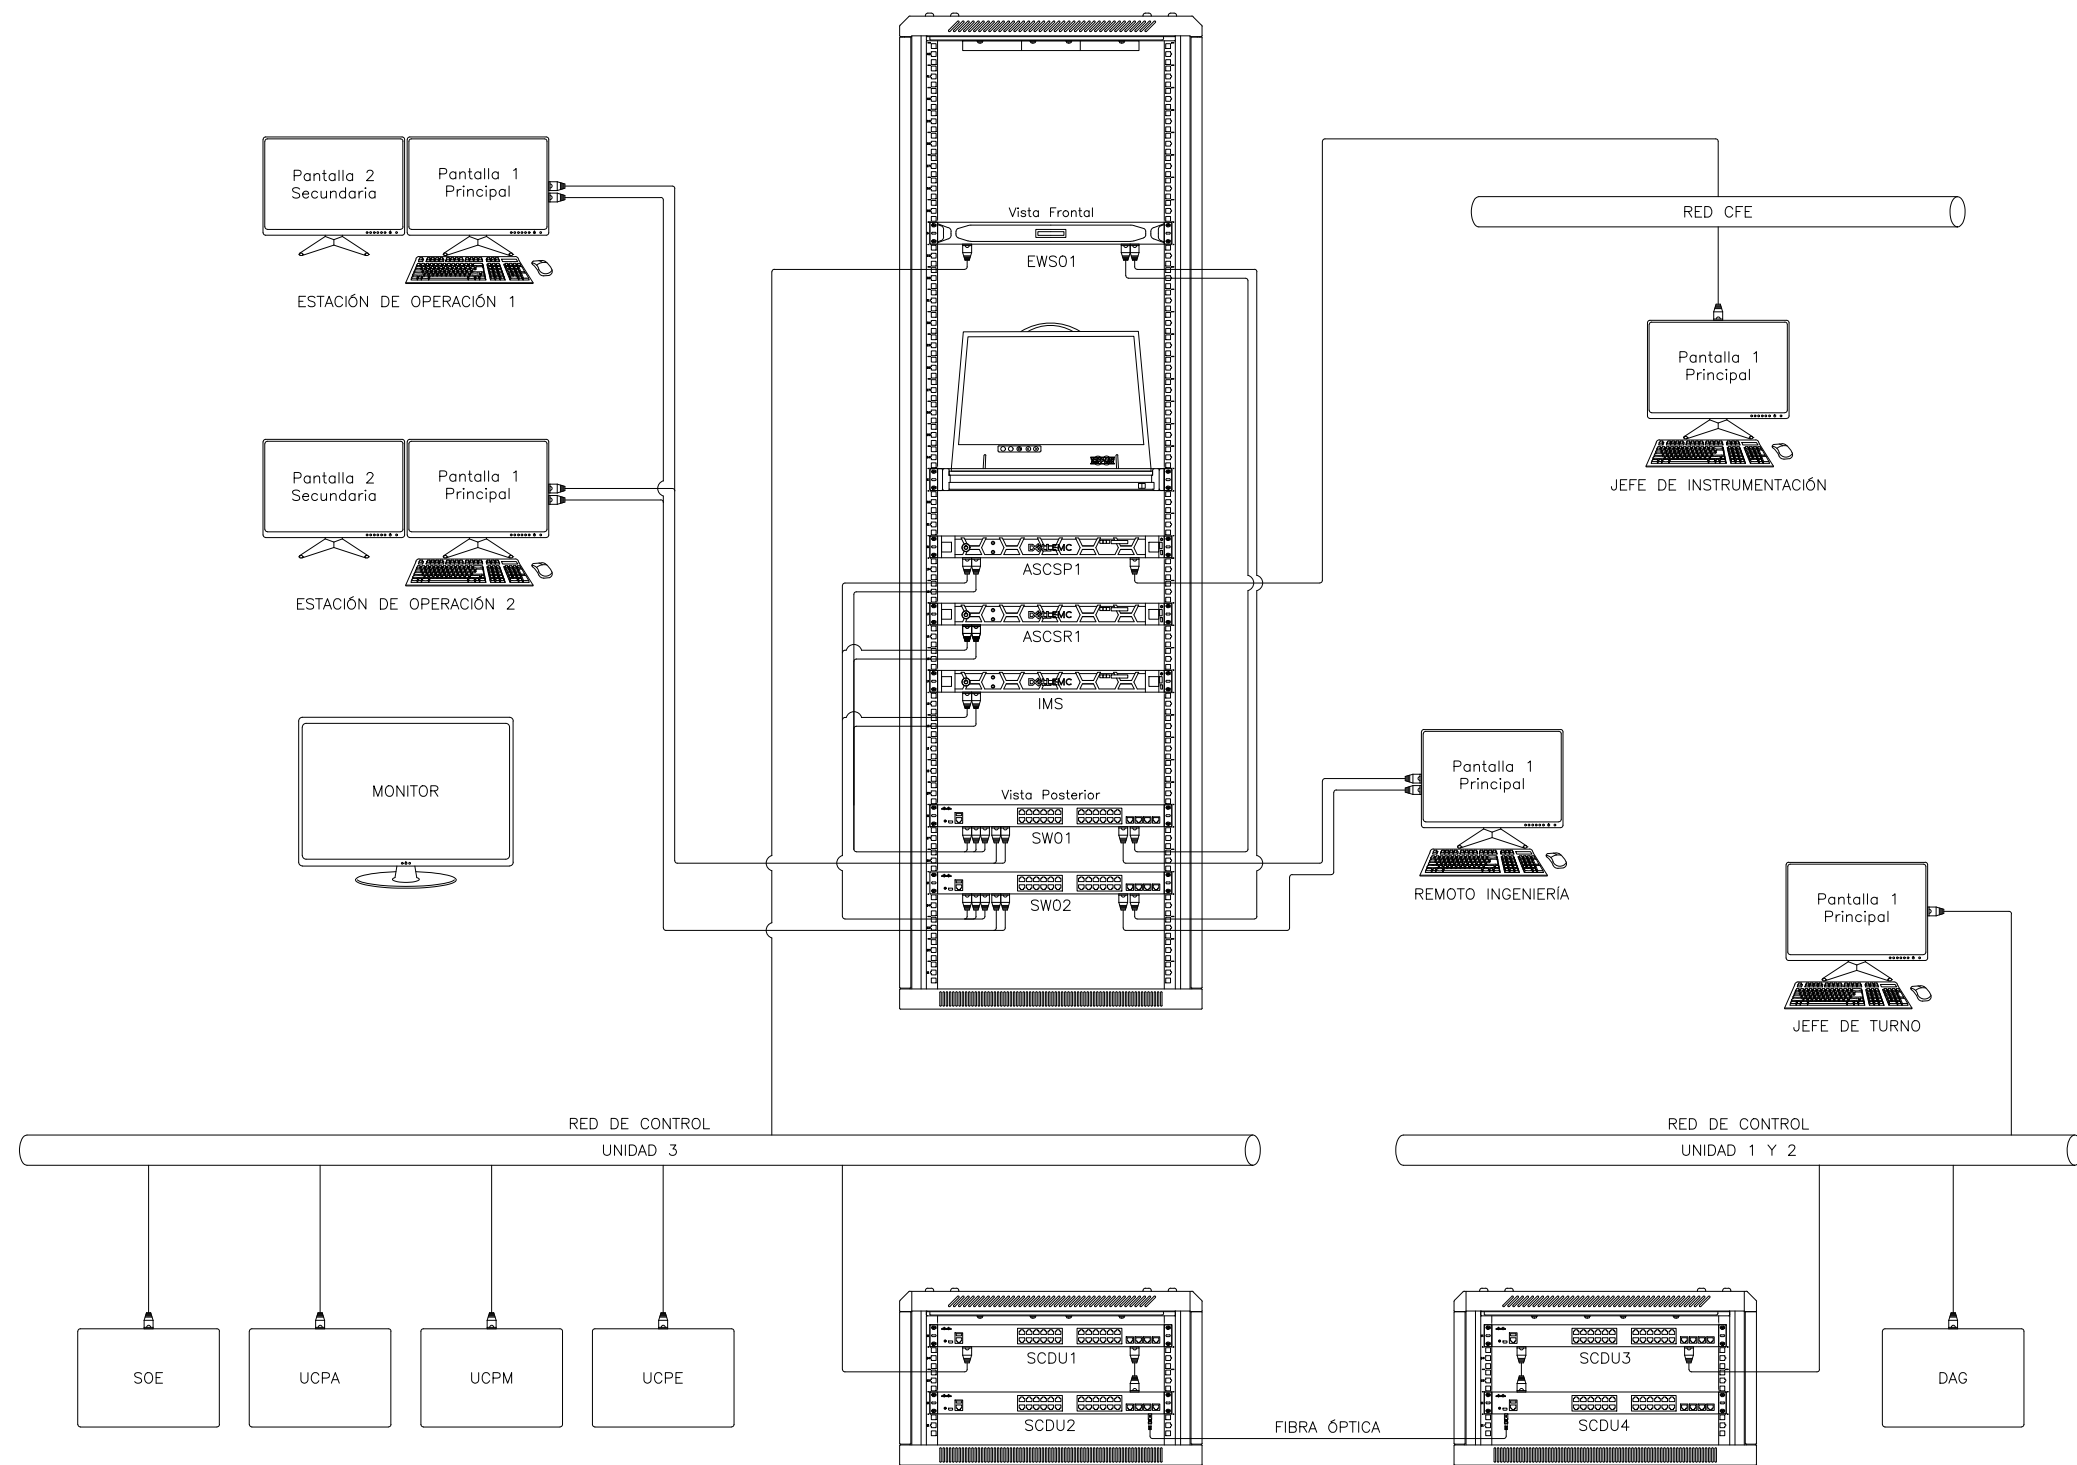

R E V I S I O N									DIBUJOS DE REFERENCIA					 Comisión Federal de Electricidad MEXICO	 INTEGRACIONES Y AUTOMATIZACIÓN HOH SA DE CV	SUMINISTRO, INSTALACIÓN, CONFIGURACIÓN Y PUESTA EN MARCHA SISTEMA DE TELECOMUNICACIONES			
REV	DESCRIPCION	DIBUJO	PROY.	REVISO	COORD.	APROBO	CLIENTE	FECHA	No. DIBUJO	DESCRIPCION	DIBUJO	REVISO	FECHA			ARQUITECTURA DE RED			
A	EMITIDO PARA DISEÑO	DMR	HPP	HGP	-	-	-	ABRIL/2023											
1	EMITIDO PARA CONSTRUCCIÓN																		
0	AS BUILT																		
														ESC: 1:30			No. DE PLANO:		REV.
														UNIDADES: MM			03 DE 04		A

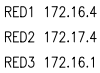

R E V I S I O N									D I B U J O S D E R E F E R E N C I A					Comisión Federal de Electricidad MEXICO INTEGRACIONES Y AUTOMATIZACIÓN HOH SA DE CV SUMINISTRO, INSTALACIÓN, CONFIGURACIÓN Y PUESTA EN MARCHA SISTEMA DE TELECOMUNICACIONES INTERCONEXION DE EQUIPOS ESC: 1:30 UNIDADES: MM No. DE PLANO: 04 DE 04 REV. A	
REV	DESCRIPCION	DIBUJO	PROY.	REVISO	COORD.	APROBO	CLIENTE	FECHA	No. DIBUJO	DESCRIPCION	DIBUJO	REVISO	FECHA		
A	EMITIDO PARA DISEÑO	DMR	HPP	HGP	-	-	-	ABRIL/2023							
1	EMITIDO PARA CONSTRUCCIÓN														
0	AS BUILT														