


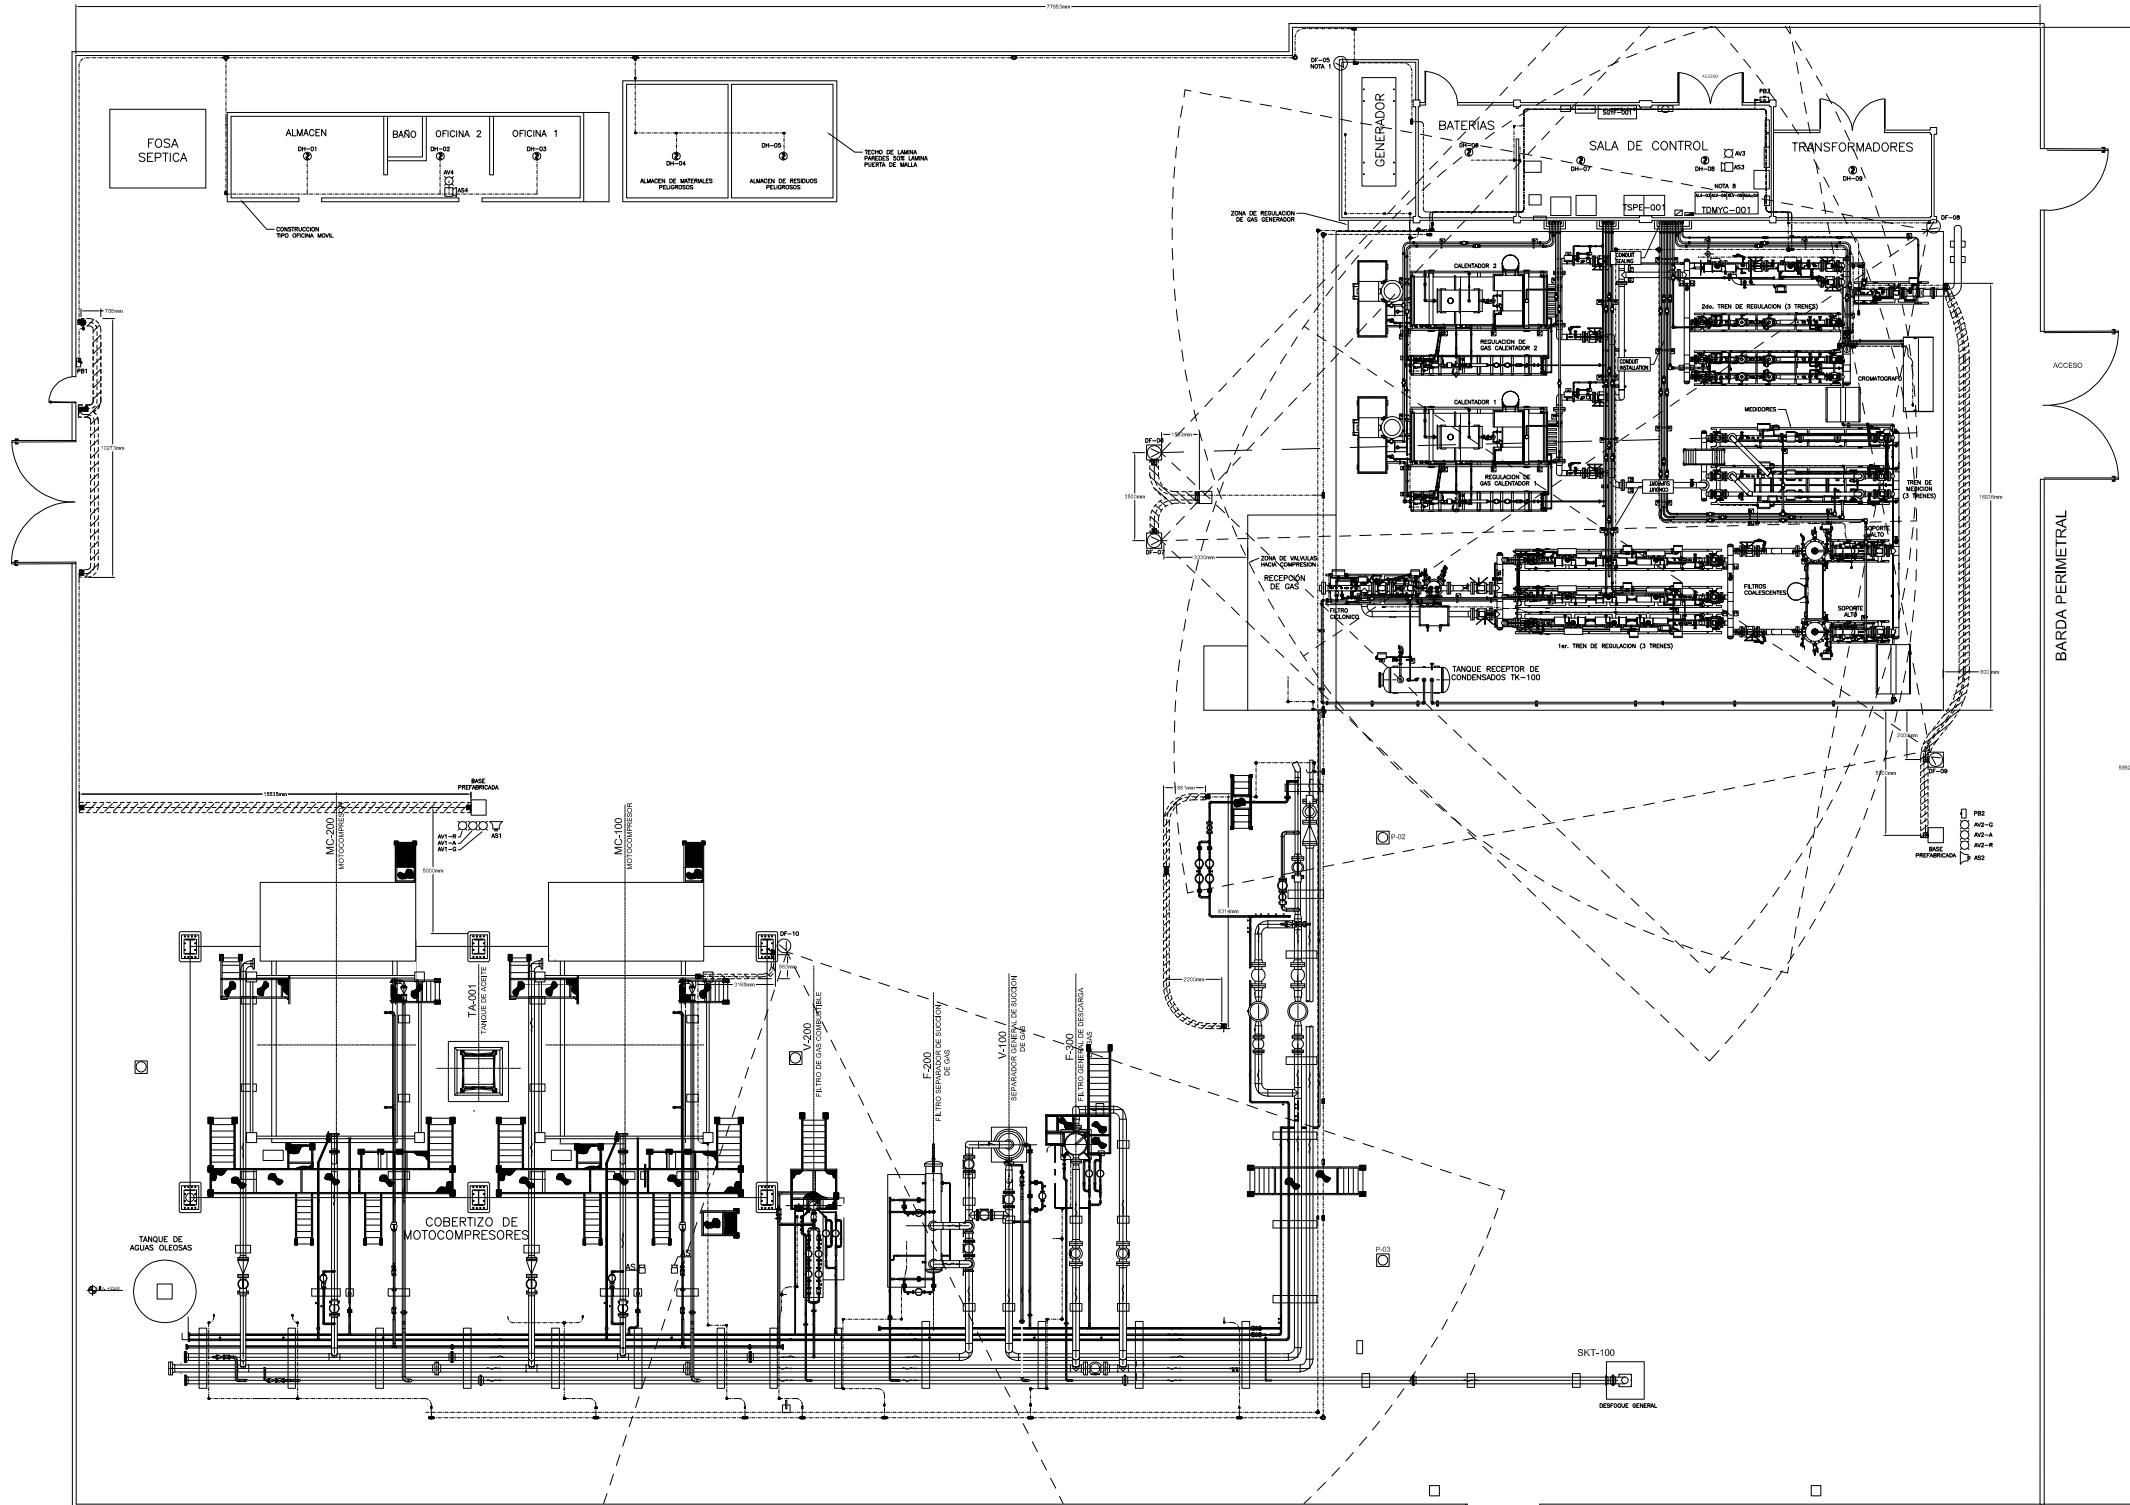

SIMBOLOGÍA	
②	DETECTOR DE HUMO
①	DETECTORES DE FUEGO
⑦	DETECTORES DE GAS
□	BOCINA INTERIORES
◁	BOCINA EXTERIORES
□	ESTACION DE BOTONES ACCIDENTE, FUGA Y FUEGO
□	SEMAFOROS INTERIORES
□	SEMAFOROS EXTERIORES
607F-001	TABLERO DE FUEGO Y GAS

NOTA 1
DETECTOR DE FUEGO EXISTENTE

NOTA 2
DETECTOR DE GAS EXISTENTE

NOTA 3
ALARMAS AUDIOVISUALES Y SONORAS EXISTENTES

INDICA CANALIZACIONES BAJO TIERRA

INDICA CANALIZACION VISIBLE

RESUMEN DE DISPOSITIVOS	
DETECTOR DE HUMO	UBICACIÓN
DH-01	ALMACÉN
DH-02	OFICINA 2
DH-03	OFICINA 1
DH-04	ALMACÉN DE MAT. PELIGROSOS
DH-05	ALMACÉN DE RESIDUOS PELIGROSOS
DH-06	SALA DE CONTROL
DH-07	SALA DE CONTROL
DH-08	TRANSFORMADORES
DH-09	TRANSFORMADORES

DETECTOR DE GAS	UBICACIÓN
DME-01	GENERADOR
DME-02	REGULACIÓN DE GAS GENERADOR
DME-03	CUARTO DE BATERÍAS (EXISTENTE)
DME-04	CALENTADOR 2
DME-05	2do. TREN DE REGULACION
DME-06	2do. TREN DE REGULACION
DME-07	2do. TREN DE REGULACION
DME-08	2do. TREN DE REGULACION
DME-09	CROMATÓGRAFO
DME-10	CALENTADOR 1
DME-11	TREN DE MEDICIÓN
DME-12	TREN DE MEDICIÓN
DME-13	TREN DE MEDICIÓN
DME-14	TREN DE MEDICIÓN
DME-15	TREN DE MEDICIÓN
DME-16	FILTROS COALEScentes
DME-17	RECEPCIÓN DE GAS
DME-18	FILTRO CICLÓNICO
DME-19	1er. TREN DE REGULACIÓN
DME-20	1er. TREN DE REGULACIÓN
DME-21	1er. TREN DE REGULACIÓN
DME-22	1er. TREN DE REGULACIÓN
DME-23	FILTROS COALEScentes
DME-24	PATIO CENTRAL
DME-25	PATIO CENTRAL
DME-26	PATIO CENTRAL
DME-27	FILTRO DE DESCARGA F-300
DME-28	SEPARADOR DE SUCCIÓN V-100
DME-29	FILTRO SEPARADOR F-200
DME-30	FILTRO DE GAS COMBUSTIBLE V-200
DME-31	FILTRO DE GAS COMBUSTIBLE V-200
DME-32	CABEZALES COMPRESOR MC-100
DME-33	CABEZALES COMPRESOR MC-100
DME-34	CABEZALES COMPRESOR MC-200
DME-35	CABEZALES COMPRESOR MC-200

DETECTOR DE FUEGO	UBICACIÓN
DF-05	GENERADOR (EXISTENTE)
DF-06	1er TREN DE REGULACIÓN
DF-07	2do TREN DE REGULACIÓN
DF-08	TREN DE MEDICIÓN
DF-09	CALENTADORES
DF-10	FILTROS COMPRESORES

ALARMAS VISUALES	UBICACIÓN
AV1-G	ENTRADA
AV1-A	ENTRADA
AV1-R	ENTRADA
AV2-G	PATIO DE VÁLVULAS
AV2-A	PATIO DE VÁLVULAS
AV2-R	PATIO DE VÁLVULAS
AV3-G	CUARTO DE CONTROL
AV3-A	CUARTO DE CONTROL
AV3-R	CUARTO DE CONTROL
AV4-G	OFICINAS
AV4-A	OFICINAS
AV4-R	OFICINAS

ALARMAS SONORAS	UBICACIÓN
AS1	ENTRADA
AS2	PATIO DE VÁLVULAS
AS3	SALA DE CONTROL
AS4	OFICINAS

BOTONERA	UBICACIÓN
PB1-A	ENTRADA
PB1-L	ENTRADA
PB1-F	ENTRADA
PB2-A	PATIO DE VÁLVULAS
PB2-L	PATIO DE VÁLVULAS
PB2-F	PATIO DE VÁLVULAS
PB3-A	CUARTO DE CONTROL
PB3-L	CUARTO DE CONTROL
PB3-F	CUARTO DE CONTROL

R E V I S I Ó N								
REV	DESCRIPCIÓN	DIBUJO	PROYECTO	REVISÓ	COORD.	APROBÓ	CLIENTE	FECHA
A	EMITIDO PARA DISEÑO	DMR	HPP	HGP	-	-	-	JUL/2020
0	EMITIDO PARA CONSTRUCCION	DMR	HPP	HGP	-	-	-	AGO/2020
1	AS BUILT	DMR	HPP	HGP	-	-	-	MAR/2021

DIBUJOS DE REFERENCIA					
No. DIBUJO	DESCRIPCION	ED	REV	FECHA	

Carretera Escénica Tijuana-Ensenada Km 82.2
CP 22760, Baja California, México.

INTEGRACIONES Y AUTOMATIZACIÓN H0H SA DE CV

SUMINISTRO, INSTALACIÓN, CONFIGURACIÓN Y PUESTA EN MARCHA DE SISTEMA DE GAS Y FUEGO EN			
LAYOUT DE TRAYECTORIA DE CANALIZACIONES			
ESC.	1:300	No. DE PLANO:	REV
ACOT. EN:	MM	01 DE 01	1