

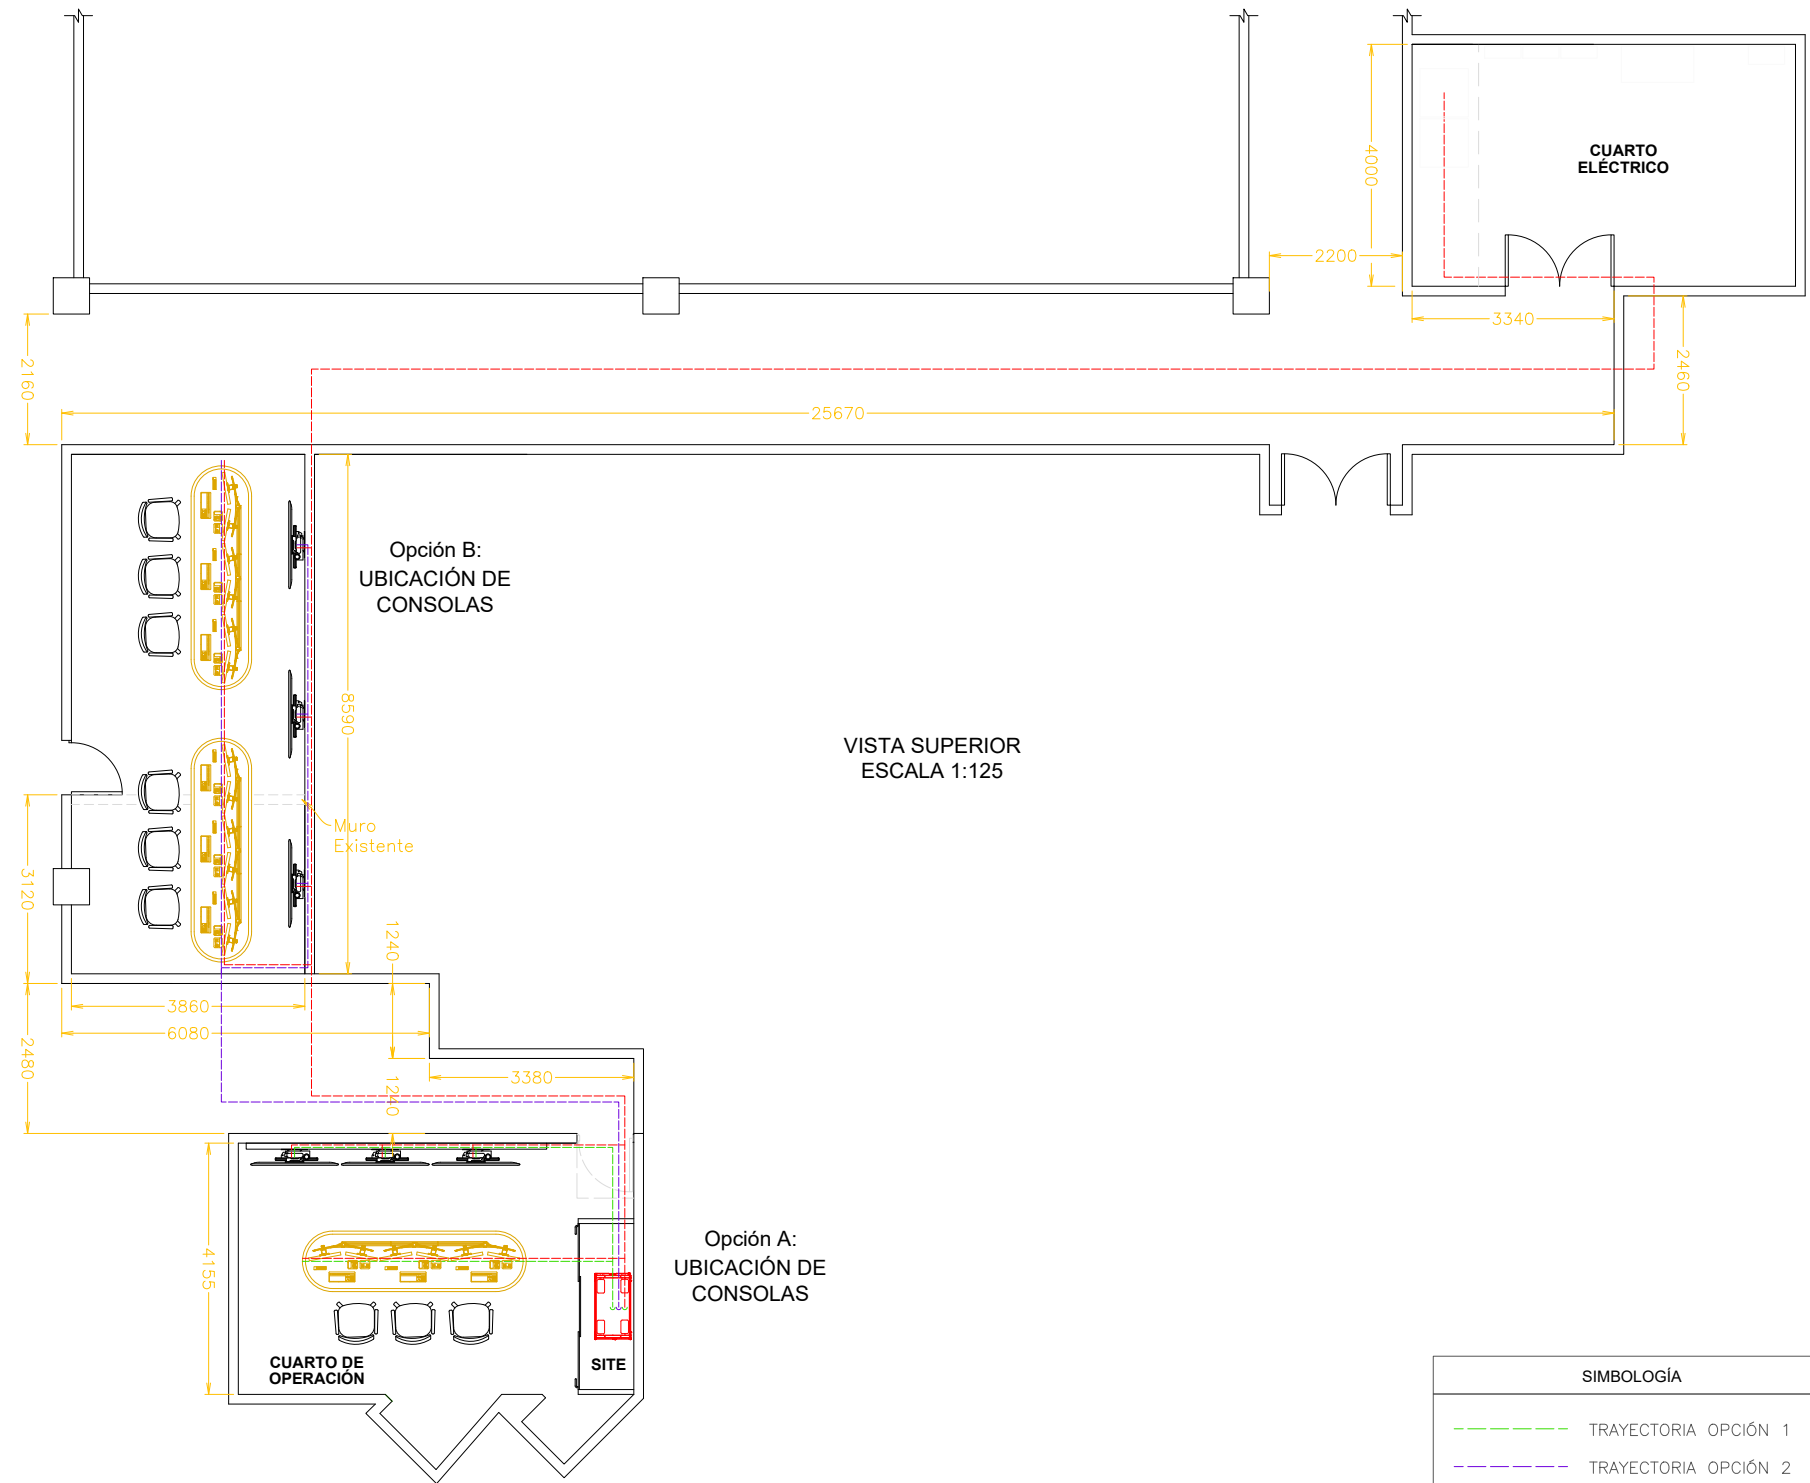


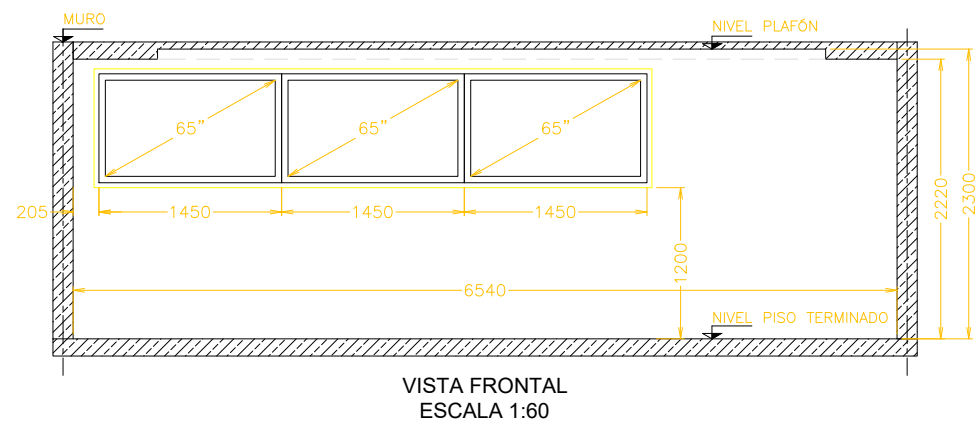

SIMBOLOGÍA	
	TRAYECTORIA OPCIÓN 1
	TRAYECTORIA OPCIÓN 2
	TRAYECTORIA ELÉCTRICO


[illegible]

APROBADO POR	
REVISÓ:	
APROBÓ:	
PEMEX LOGÍSTICA SUBDIRCCIÓN DE TRANSPORTE	

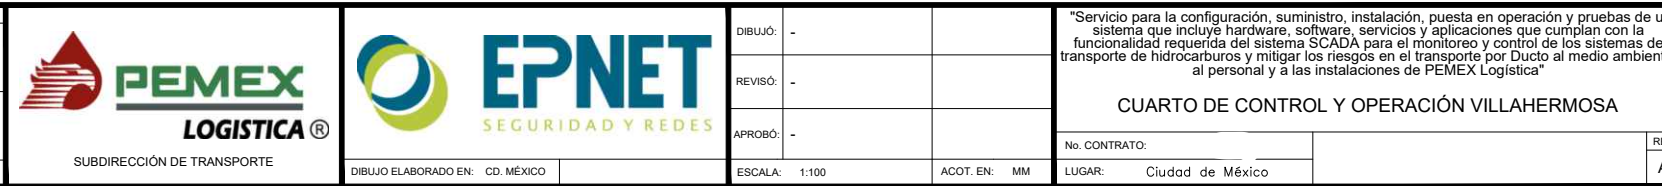




DETALLE DEL CUARTO DE OPERACIÓN

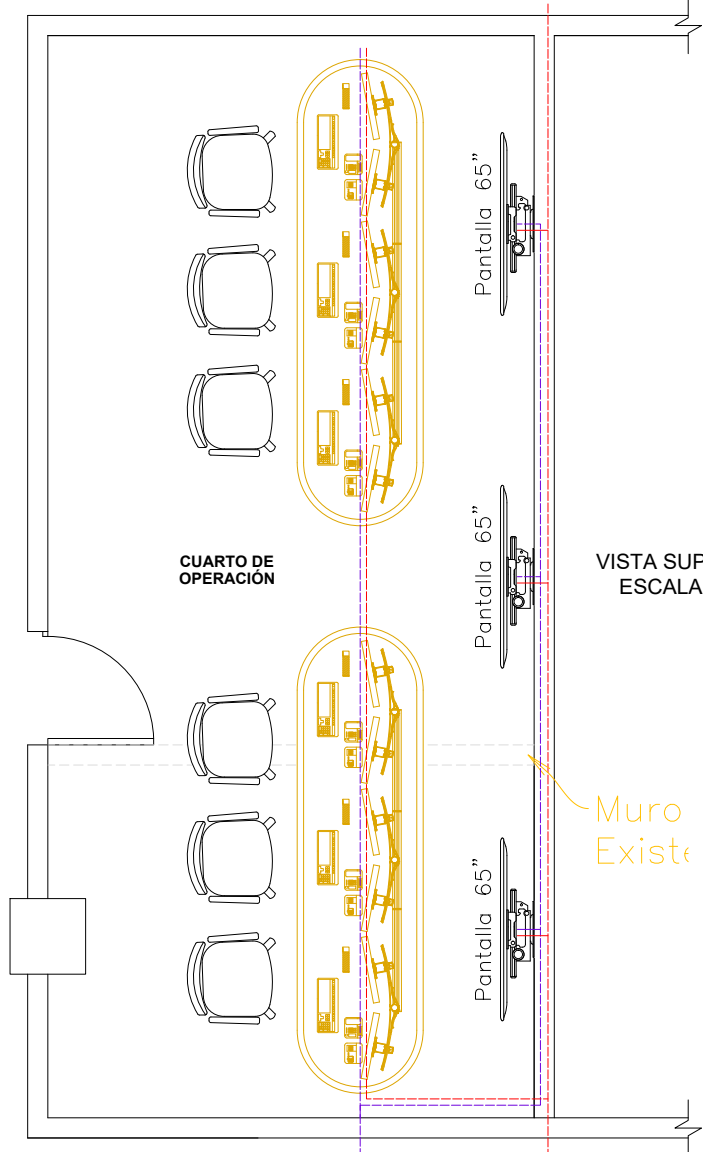

VISTA SUPERIOR
ESCALA 1:60


Muro
Existe

MURO

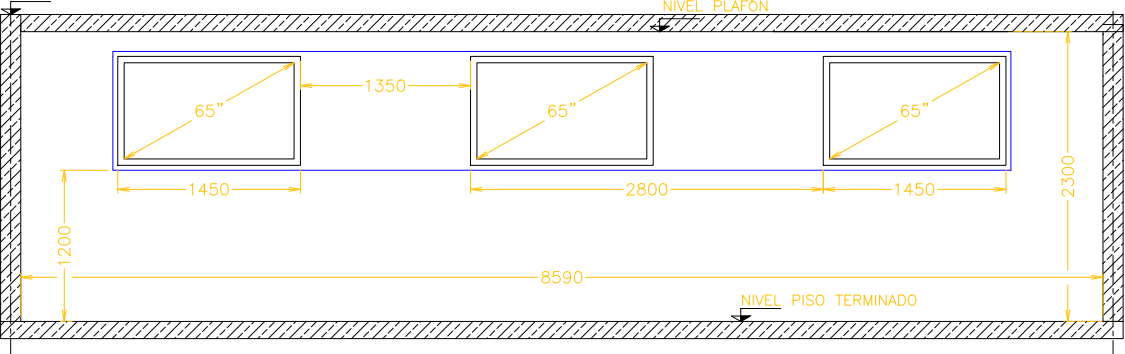

VISTA LATERAL
ESCALA 1:60

SUBGERENCIA DE PROGRAMACIÓN Y ENLACE CORPORATIVO

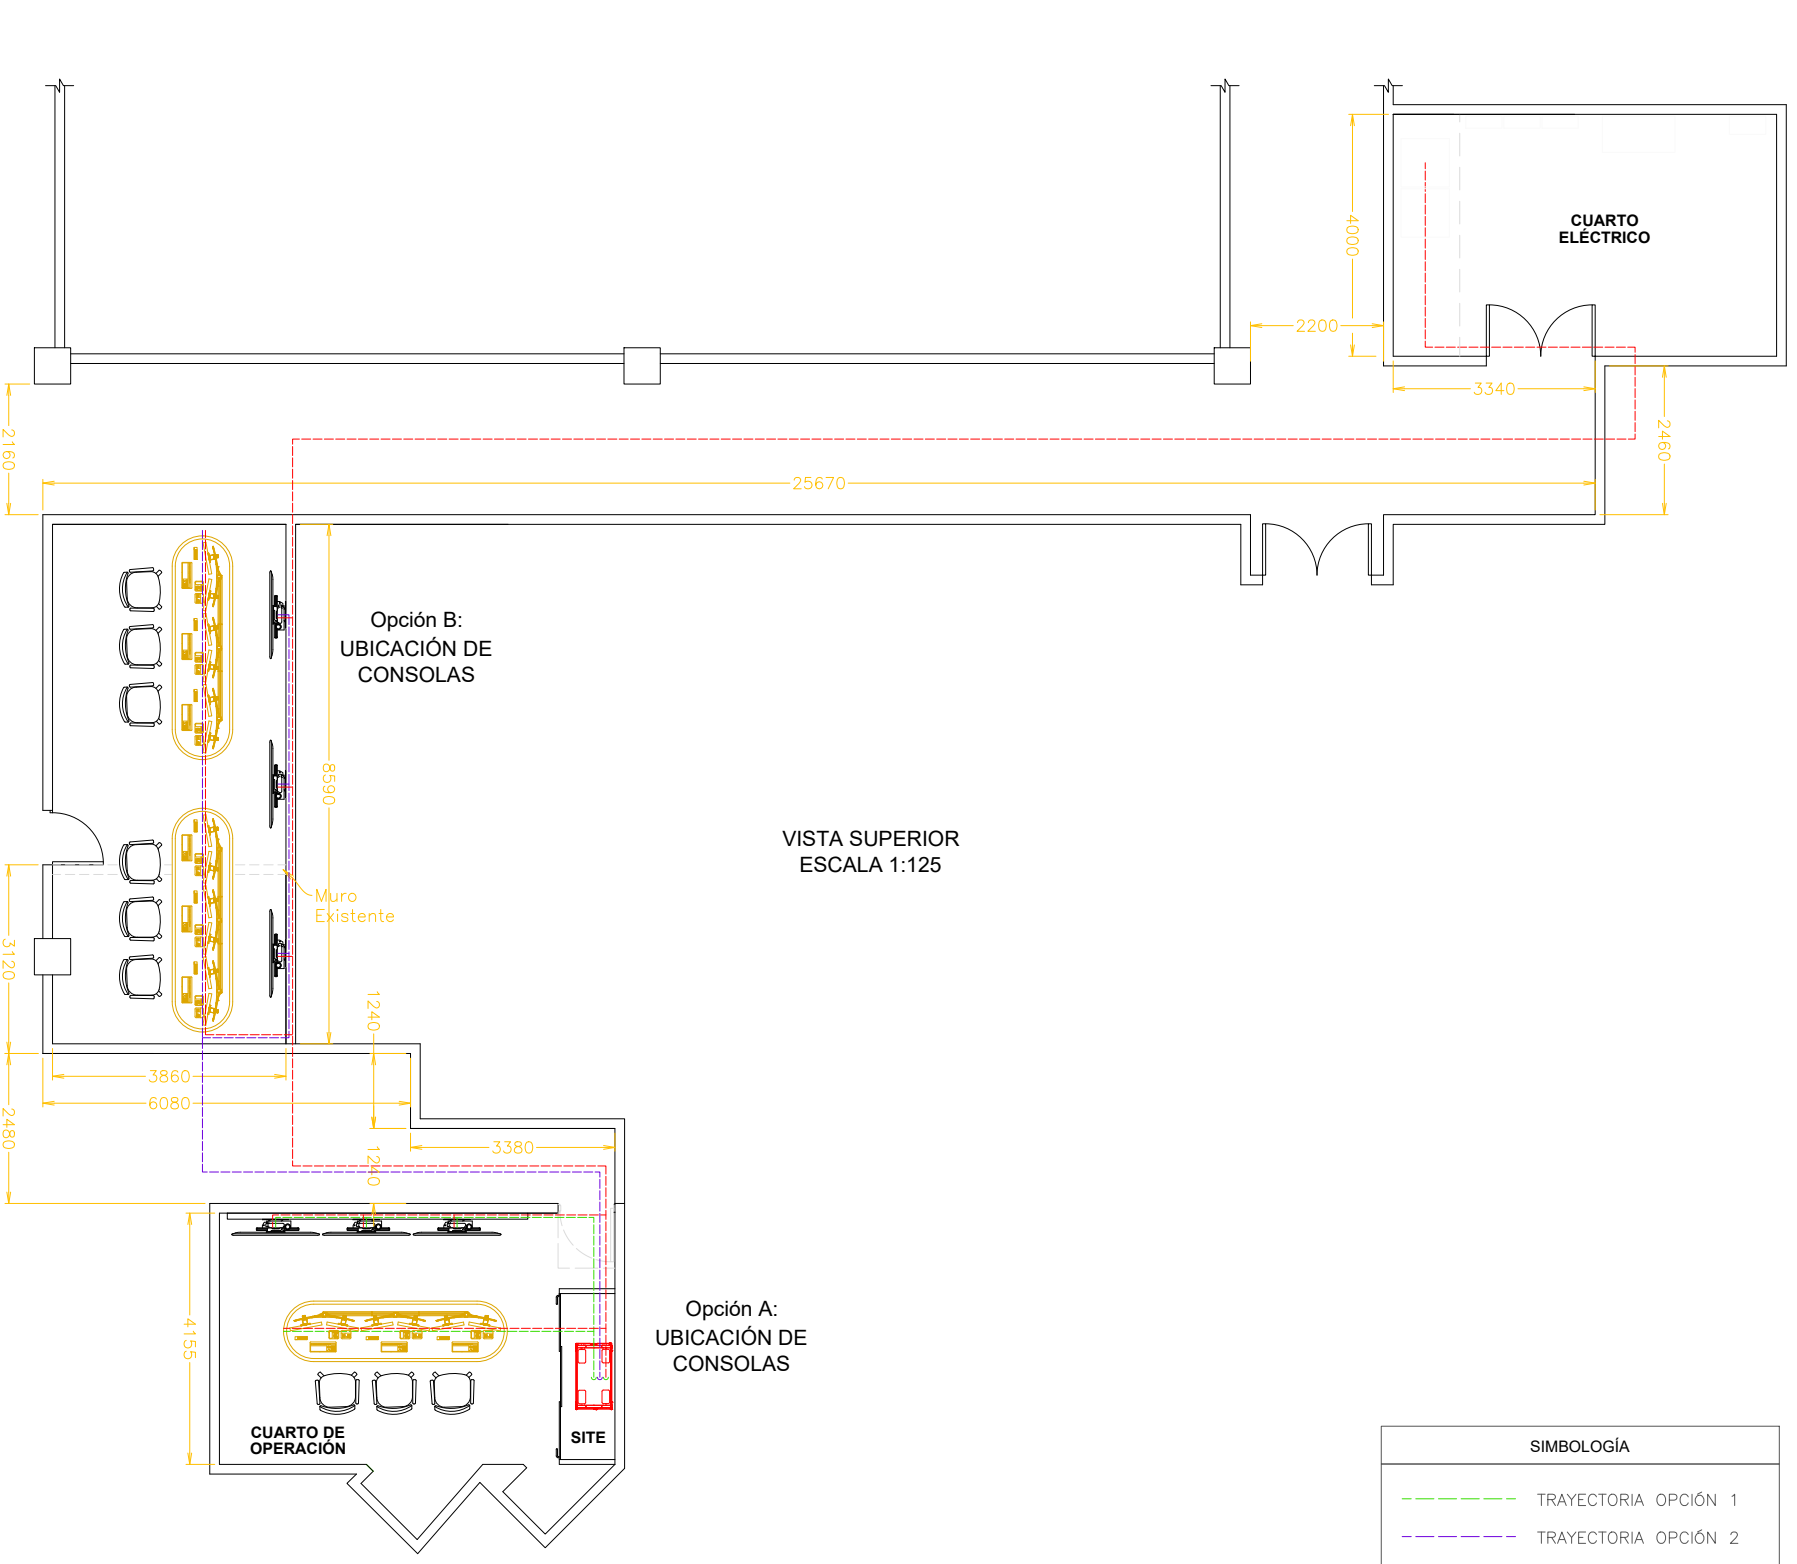

VISTA SUPERIOR
ESCALA 1:125

Opción A:
UBICACIÓN DE
CONSOLAS

Opción B:
UBICACIÓN DE
CONSOLAS

Muro
Existente

SIMBOLOGÍA

- TRAYECTORIA OPCIÓN 1
- TRAYECTORIA OPCIÓN 2
- TRAYECTORIA ELÉCTRICO

CP	FECHA	MCA.	REVISIONES				NUM.	DIBUJOS DE REFERENCIA
			DESCRIPCIÓN	FECHA	POR	VoBo		
		A	Preliminar	07-Mar-2024				

APROBADO POR	
REVISÓ:	
APROBÓ:	
PEMEX LOGÍSTICA SUBDIRECCIÓN DE TRANSPORTE	



SUBDIRECCIÓN DE TRANSPORTE



SEGURIDAD Y REDES

DIBUJO ELABORADO EN: CD. MÉXICO

DIBUJÓ:	-
REVISÓ:	-
APROBÓ:	-
ESCALA:	1:100
ACOT. EN:	MM

"Servicio para la configuración, suministro, instalación, puesta en operación y pruebas de un sistema que incluye hardware, software, servicios y aplicaciones que cumplan con la funcionalidad requerida del sistema SCADA para el monitoreo y control de los sistemas de transporte de hidrocarburos y mitigar los riesgos en el transporte por Ducto al medio ambiente, al personal y a las instalaciones de PEMEX Logística"

CUARTO DE CONTROL Y OPERACIÓN VILLAHERMOSA

No. CONTRATO: LUGAR: Ciudad de México

REV A