
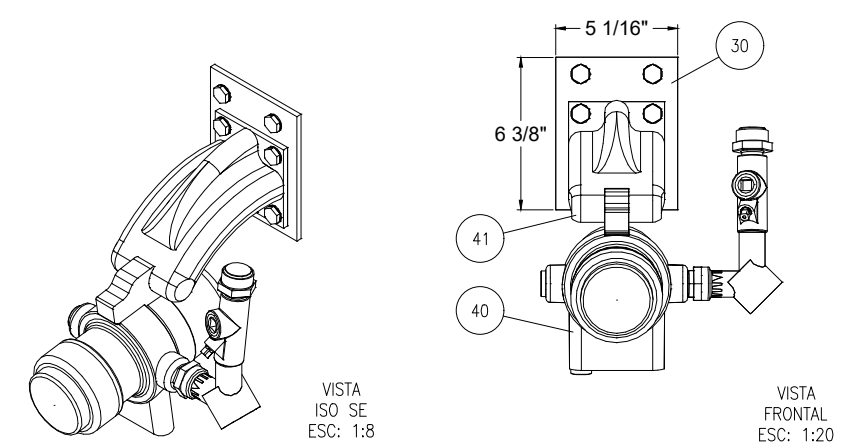
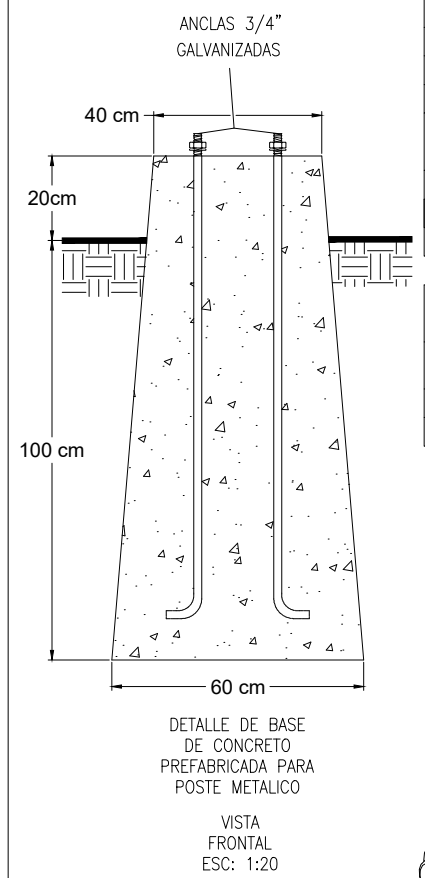
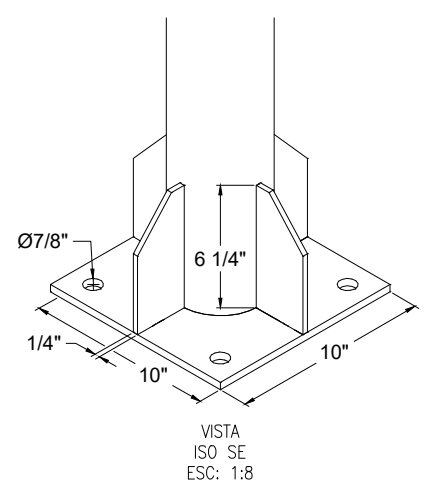
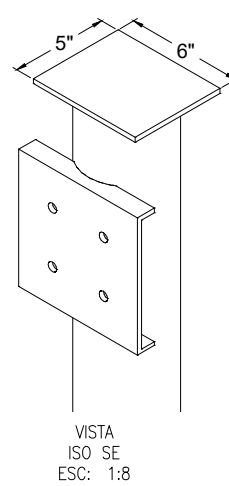
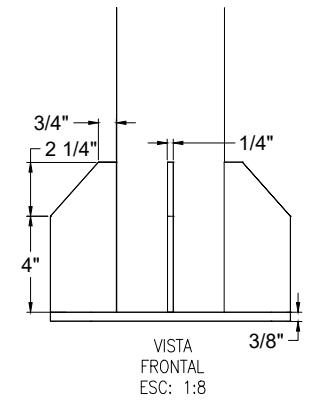
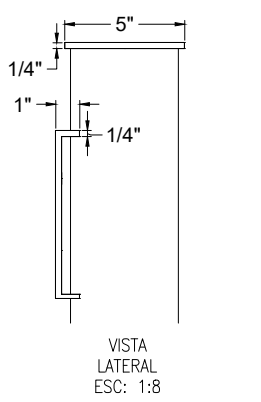
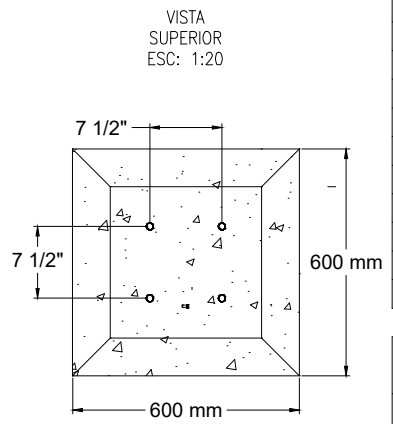
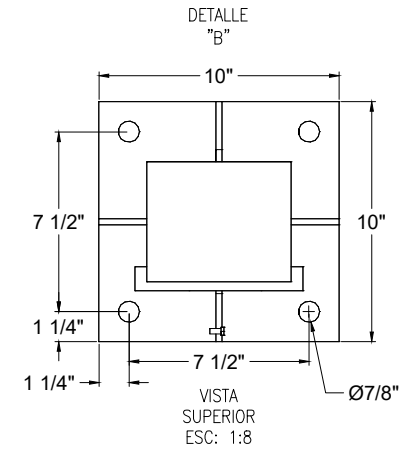
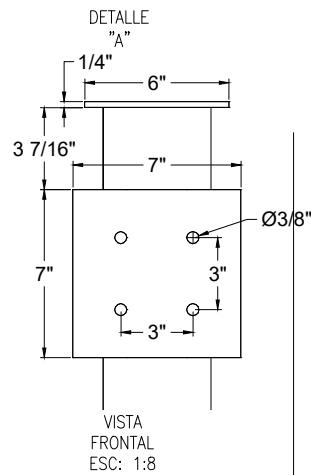


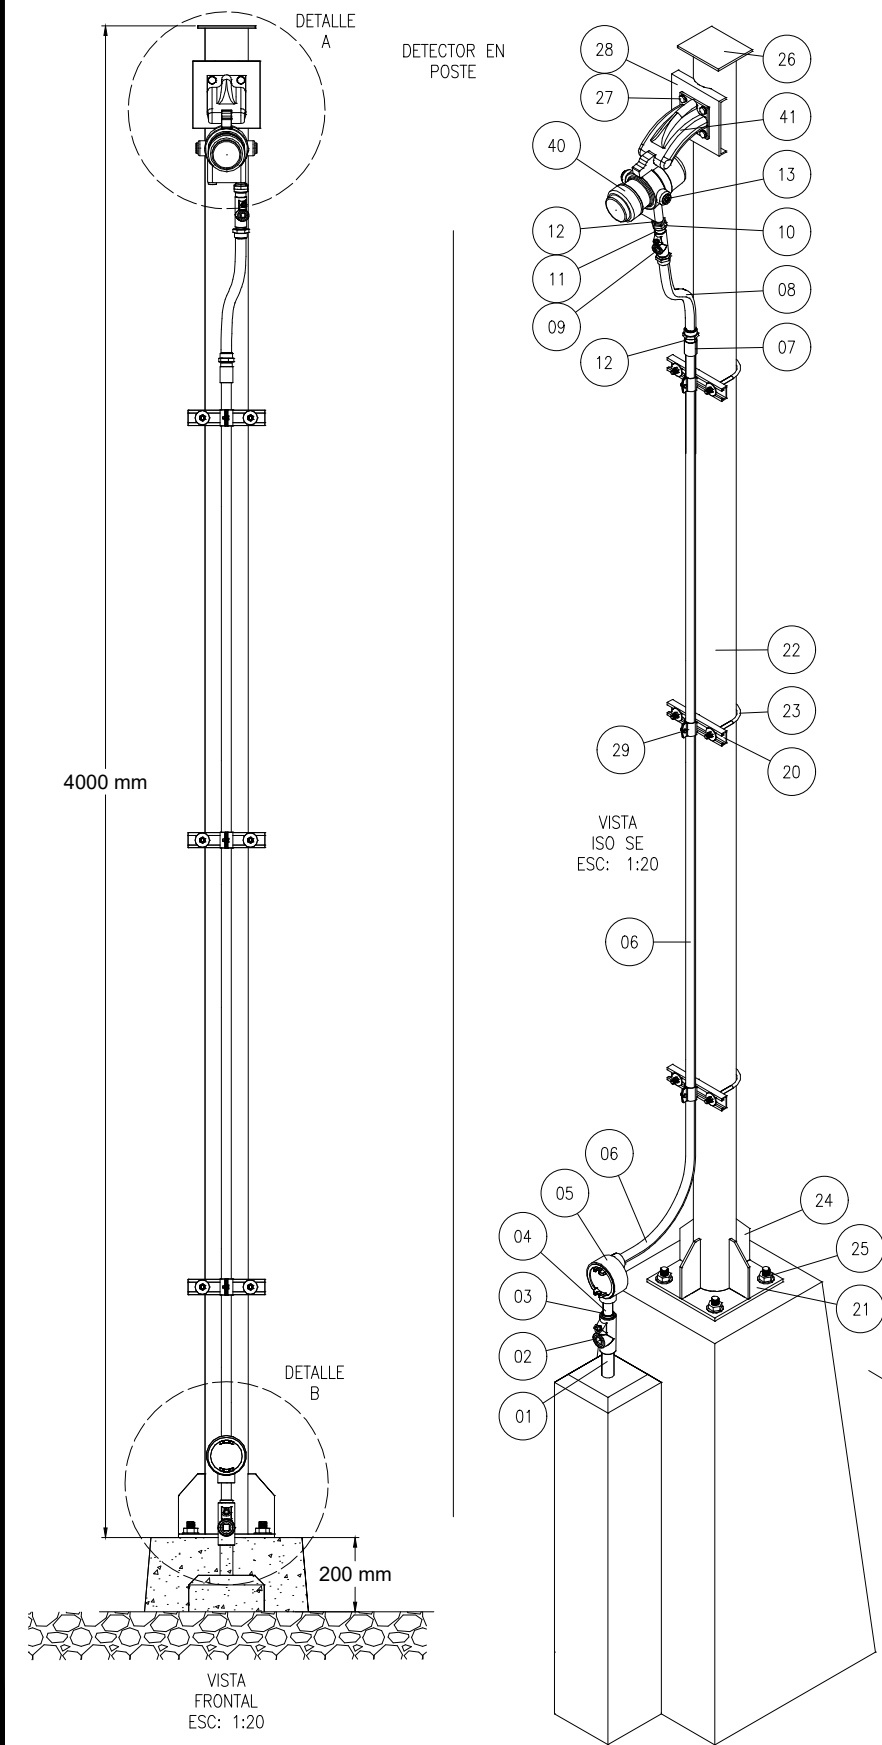

DETECTOR EN CUARTO DE CROMATÓGRAFO

LISTA DE MATERIALES

PARTE	CANT.	DESCRIPCION	MODELO	MARCA
01	01	TUBO DE ALUMINIO 1"	- - -	- - -
02	01	SELLO 1"	EYM100-A	APPLETON
03	01	REDUCCIÓN DE 1" A 3/4"	RE-21	CROUSE HINDS
04	01	NIPLE DE 3/4"	NIPLE-2 L	COUSE HINDS
05	01	CONDULET DE ALUMINIO APEX DE 3/4" TIPO "B"	GRUB 75-A	APPLETON
06	REQ	TUBO DE ALUMINIO 3/4"	- - -	RAWELT
07	01	COPLE DE ALUMINIO 3/4"	- - -	RAWELT
08	01	COPLE FLEXIBLE APEX DE 1/2" X 18"	ECGJH 118	CROUSE HINDS
09	01	SELLO DE ALUMINIO 1/2"	EYS-11	CROUSE HINDS
10	01	TUERCA UNIÓN MACHO - HEMBRA 1/2"	UNY-105 SA	CROUSE HINDS
11	01	NIPLE DE ALUMINIO 1/2"	NIPLE-2 L	CROUSE HINDS
12	02	REDUCCIÓN BUSHING DE 3/4" a 1/2"	RE-31	CROUSE HINDS
13	03	TAPÓN DE ALUMINIO DE 3/4"	PLG-2	CROUSE HINDS

LISTA DE ACCESORIOS

PARTE	CANT.	DESCRIPCION	MODELO	MARCA
20	03	UNICANAL 4 X 2"	- - -	ANCLO
21	01	PLACA DE ACERO DE 10" X 10" X 3/8"	- - -	- - -
22	01	TUBO DE ACERO DE 4" CED. 40	- - -	- - -
23	03	ABRAZADERA TIPO "U" DE 4"	- - -	ANCLO
24	04	CARTABÓN DE PLACA DE ACERO DE 5-1/2" X 2" X 1/4"	- - -	- - -
25	REQ	JUEGO DE TUERCAS Y ARANDELA PLANA DE 3/4"Ø C. STD.	- - -	- - -
26	01	PLACA DE ACERO DE 6" X 5" X 1/4"	- - -	- - -
27	REQ	JUEGO DE TORNILLOS DE 5/16" X 1-1/2" LONG. CON TUERCAS Y ARANDELA PLANA CUERDA STD.	- - -	- - -
28	01	PLACA DE ACERO DE 7" X 7" X 1/4"	- - -	- - -
29	03	ABRAZADERA 3/4" PARA UNICANAL	- - -	ANCLO
30	03	PLACA DE 6-3/8" X 5-1/16" X 1/4"	- - -	- - -

LISTA DE EQUIPOS

ITEMS	CANT.	DESCRIPCION	MODELO	MARCA
40	01	DETECTOR DE FUEGO IR MULTIESPECTRO	X3301	DET-TRONICS
41	01	SOPORTE DEL DETECTOR (BRAZO)	Q9033A	DET-TRONICS

R E V I S I O N									DIBUJOS DE REFERENCIA					 GASODUCTO AGUAPRIETA GASODUCTO – EL CARRIZO	 HOH INTEGRACIONES Y AUTOMATIZACIÓN HOH SA DE CV	"SUMINISTRO, INSTALACIÓN, CONFIGURACIÓN Y PUESTA EN MARCHA DE SISTEMA DE GAS Y FUEGO"		
REV	DESCRIPCION	DIBUJO	PROY.	REVISO	COORD.	APROBO	CLIENTE	FECHA	No. DIBUJO	DESCRIPCION	DIBUJO	REVISO	FECHA			TÍPICO DE INSTALACIÓN DE DETECTOR DE FUEGO		
A	EMITIDO PARA DISEÑO	DMR	HPP	HGP	–	–	–	FEB/2022										
1	EMITIDO PARA CONSTRUCCIÓN																	
0	AS BUILT																	
														ESC: 1:8, 1:20	No. DE PLANO:	REV.		
														UNIDADES: PLG	01 DE 01	A		